


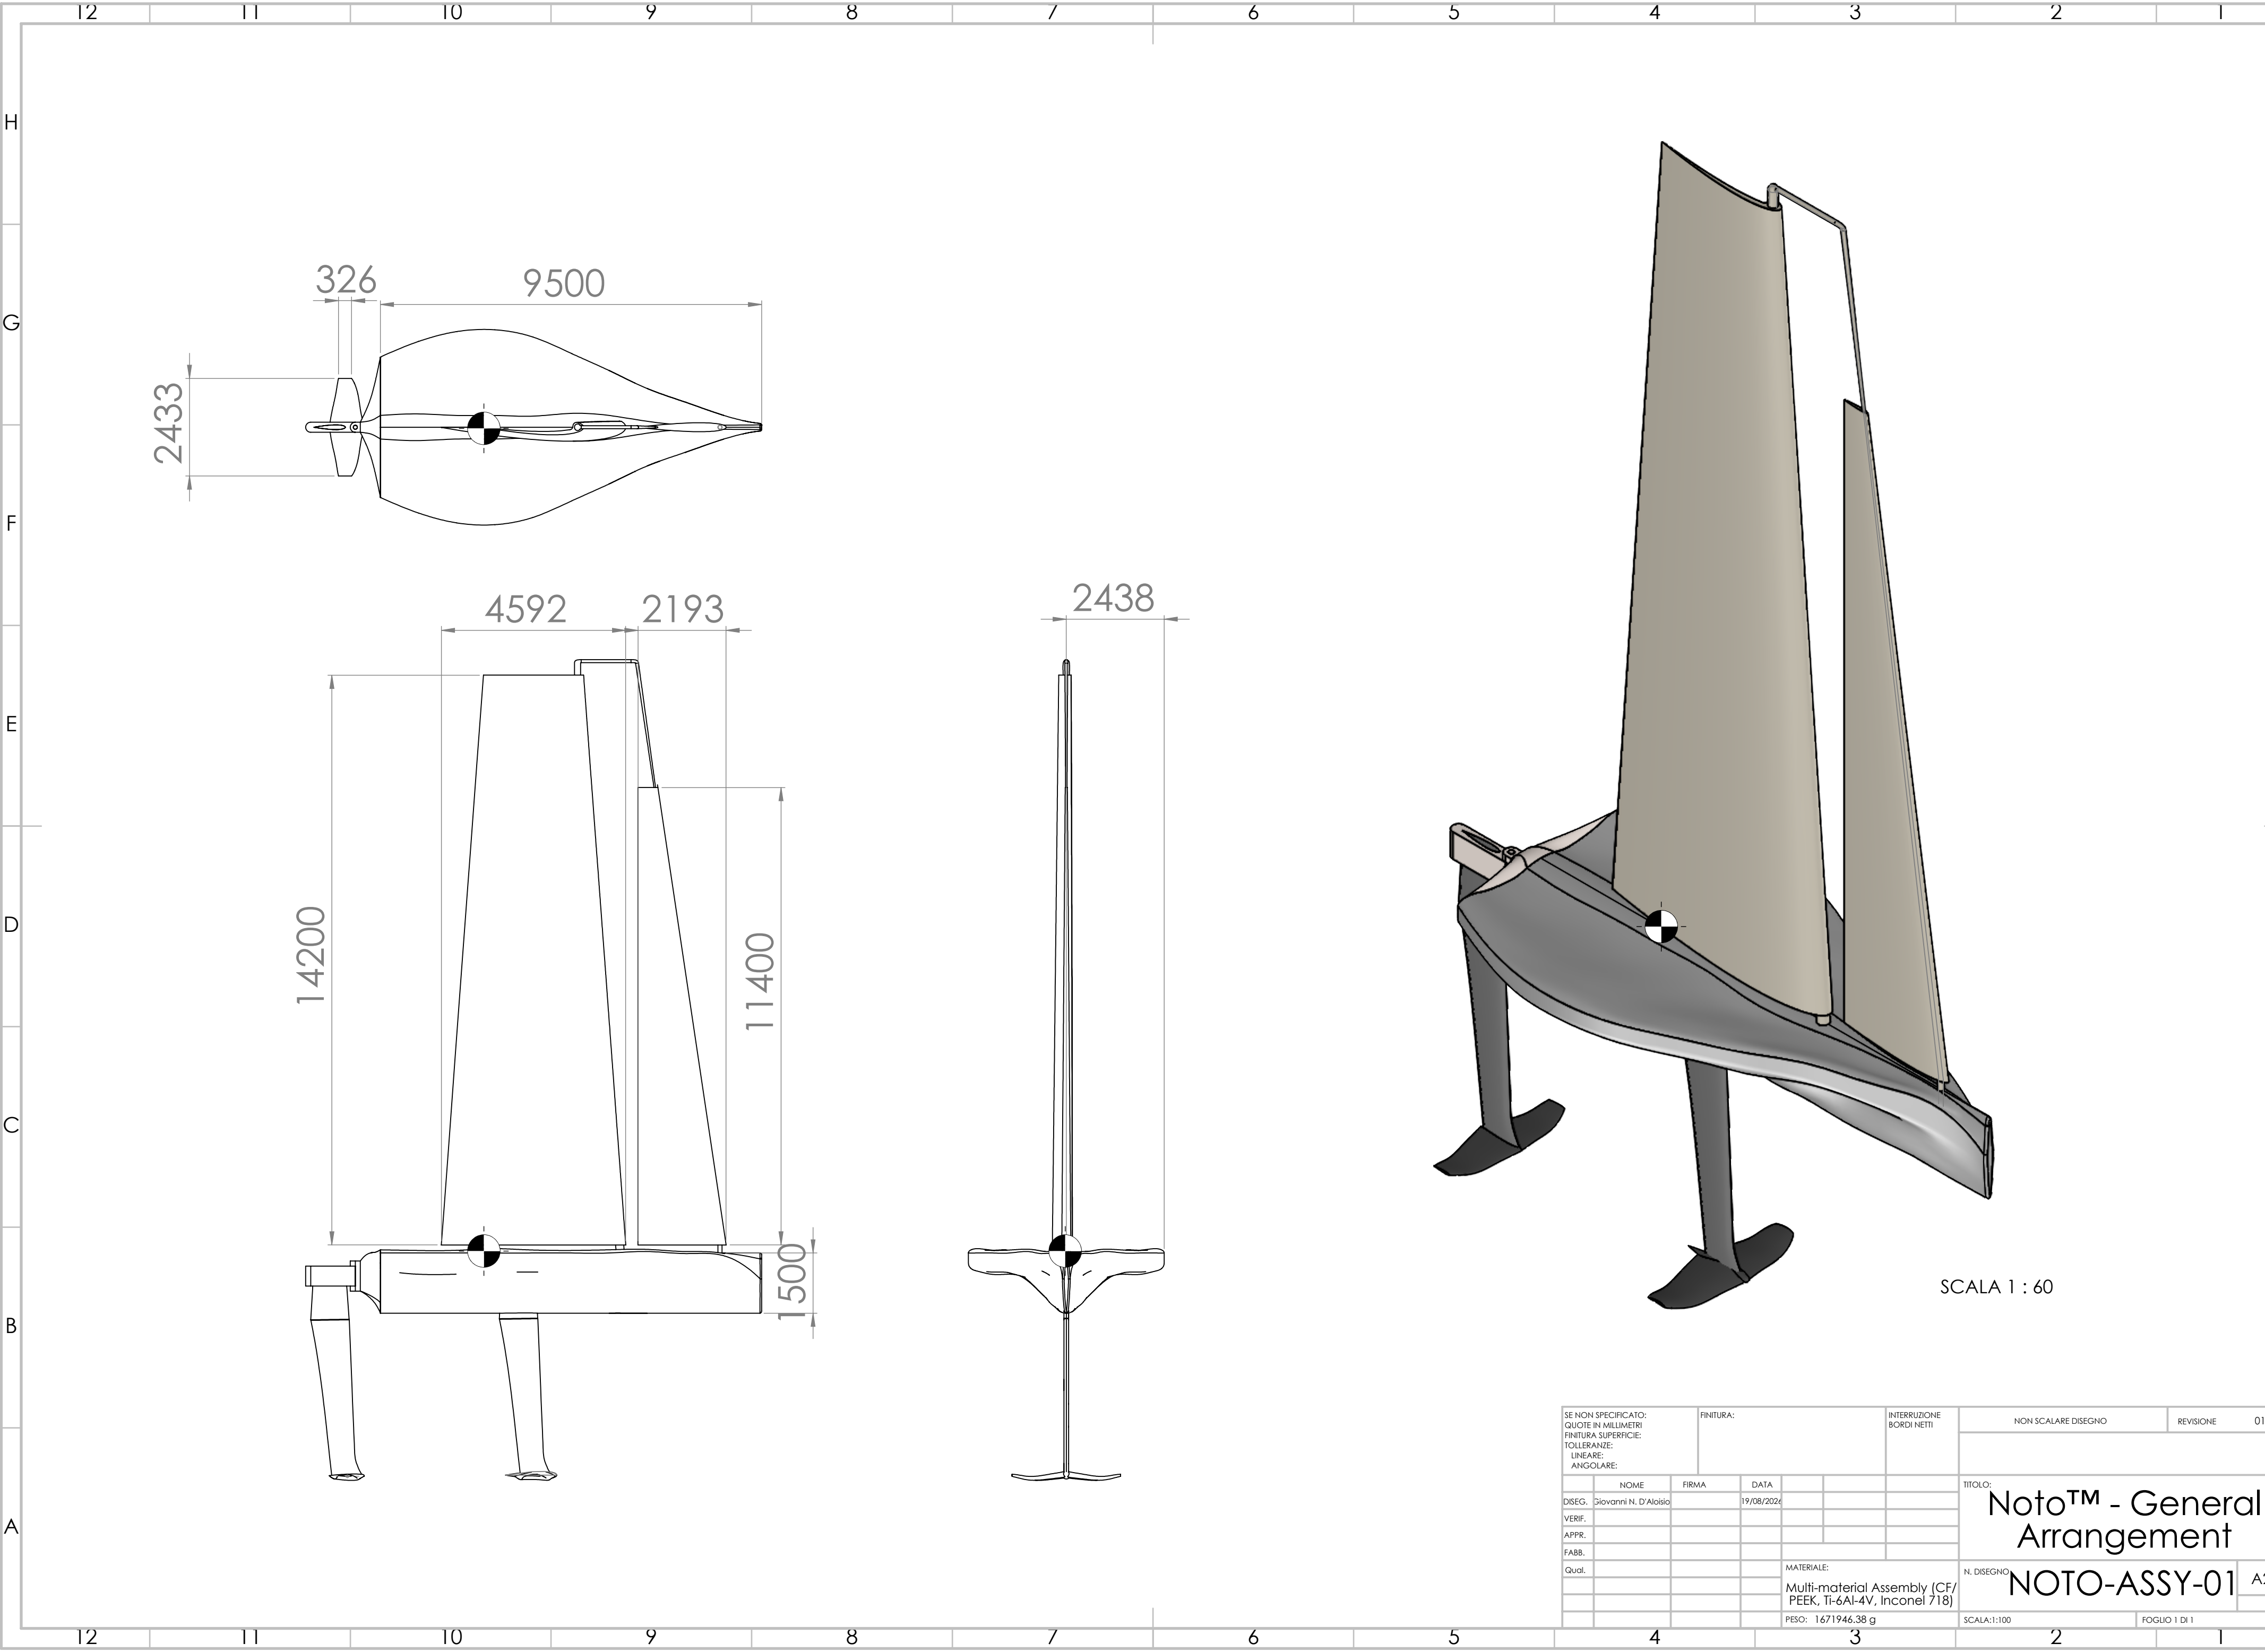

SCALA 1 : 60

SE NON SPECIFICATO: QUOTE IN MILLIMETRI FINITURA SUPERFICIE: TOLLERANZE: LINEARE: ANGOLARE:			FINITURA:		INTERRUZIONE BORDI NETTI		NON SCALARE DISEGNO		REVISIONE		01				
	NOME		FIRMA		DATA								TITOLO: Noto™ - General Arrangement		
DISEG.	Giovanni N. D'Aloisio				19/08/2024										
VERIF.															
APPR.															
FABB.															
Qual.													N. DISEGNO NOTO-ASSY-01		
												A2			